
附錄二(設計圖說)

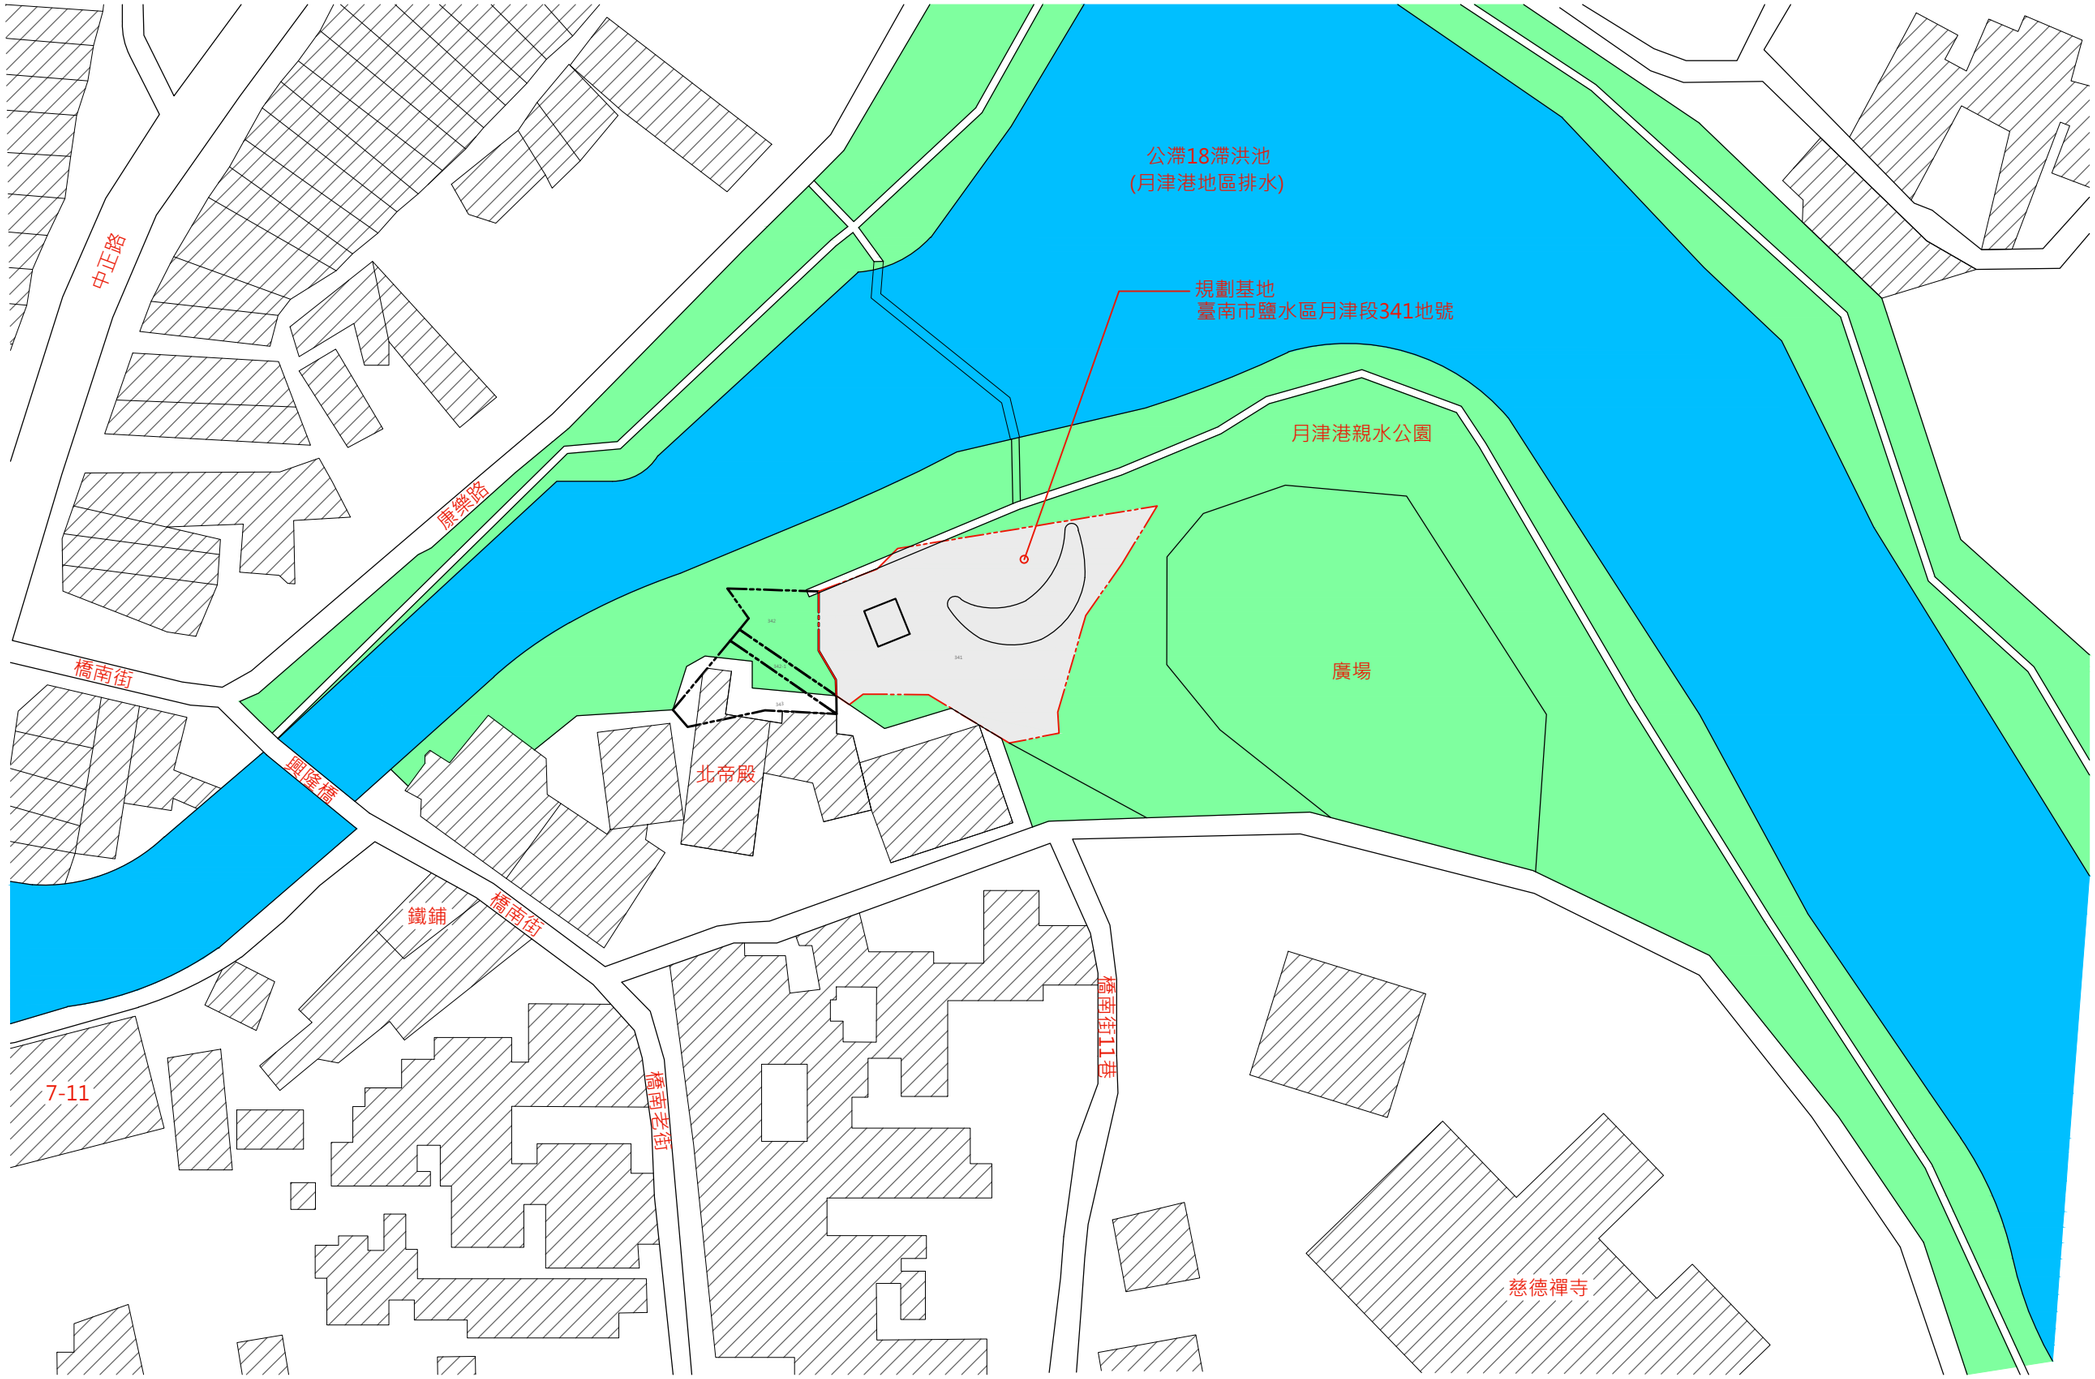

月津港親水公園區域平面圖
A3: S=1/800

羊門設計與建築
Sheepgate Design & Architecture
+
羊門工程行

地址: 台南市崇善12街6巷15弄2號
Tel: 06-2600846

PROJECT TITLE 案名
臺南市鹽水區
月津港公園公共廁所新建工程

PROJECT NO. 案號
2024-08

SHEET NAME 圖名
月津港親水公園區域平面圖

DRAWN NO. 圖號
A2-0

SCALE 比例
A3
S:1/800
cm

DATE 日期
202408

REVIEWED 審核確認

CLENT COMFIRM 客戶確認

SHEET NO. 頁碼
--

This drawing is copyright
本圖版權所有

公滯18滯洪池
(月津港地區排水)

人行步道
(水泥粉刷面)

管理員
崗哨

+10
+0
+0
+0
+10
+0
+60
+350
+10
+10

現有涼亭

342
342-1
341
343

現有公廁

現有鄰房

鋼浪板+金屬烤漆包版

屋頂造型意象:
鹽水港因地形略微彎曲，狀似新月
故有「月津」、「月港」之雅稱
採月亮造型屋頂呼應當地地名意象

屋頂下廊道燈具T5(2尺+4尺)

燈具造型意象:
利用燈管放射狀排列，塑造出煙火放射狀的感覺(鹽水蜂炮)

原涼亭屋面更換
面貼太陽能鈣鈦礦光電板

臺南市鹽水區月津段341地號地界

N

月津港親水公園廁所屋頂平面圖
A3: S=1/150

羊門設計與建築
Sheepgate Design & Architecture
+
羊門工程行

地址: 台南市崇善12街6巷15弄2號
Tel: 06-2600846

PROJECT TITLE 案名
臺南市鹽水區
月津港公園公共廁所新建工程

PROJECT NO. 案號
2024-08

SHEET NAME 圖名
月津港親水公園廁所屋頂平面圖

DRAWN NO. 圖號
A2-2

SCALE 比例
A3
S:1/150
cm


DATE 日期
202408

REVIEWED 審核確認

CLENT COMFIRM 客戶確認

SHEET NO. 頁碼
--

This drawing is copyright
本圖版權所有

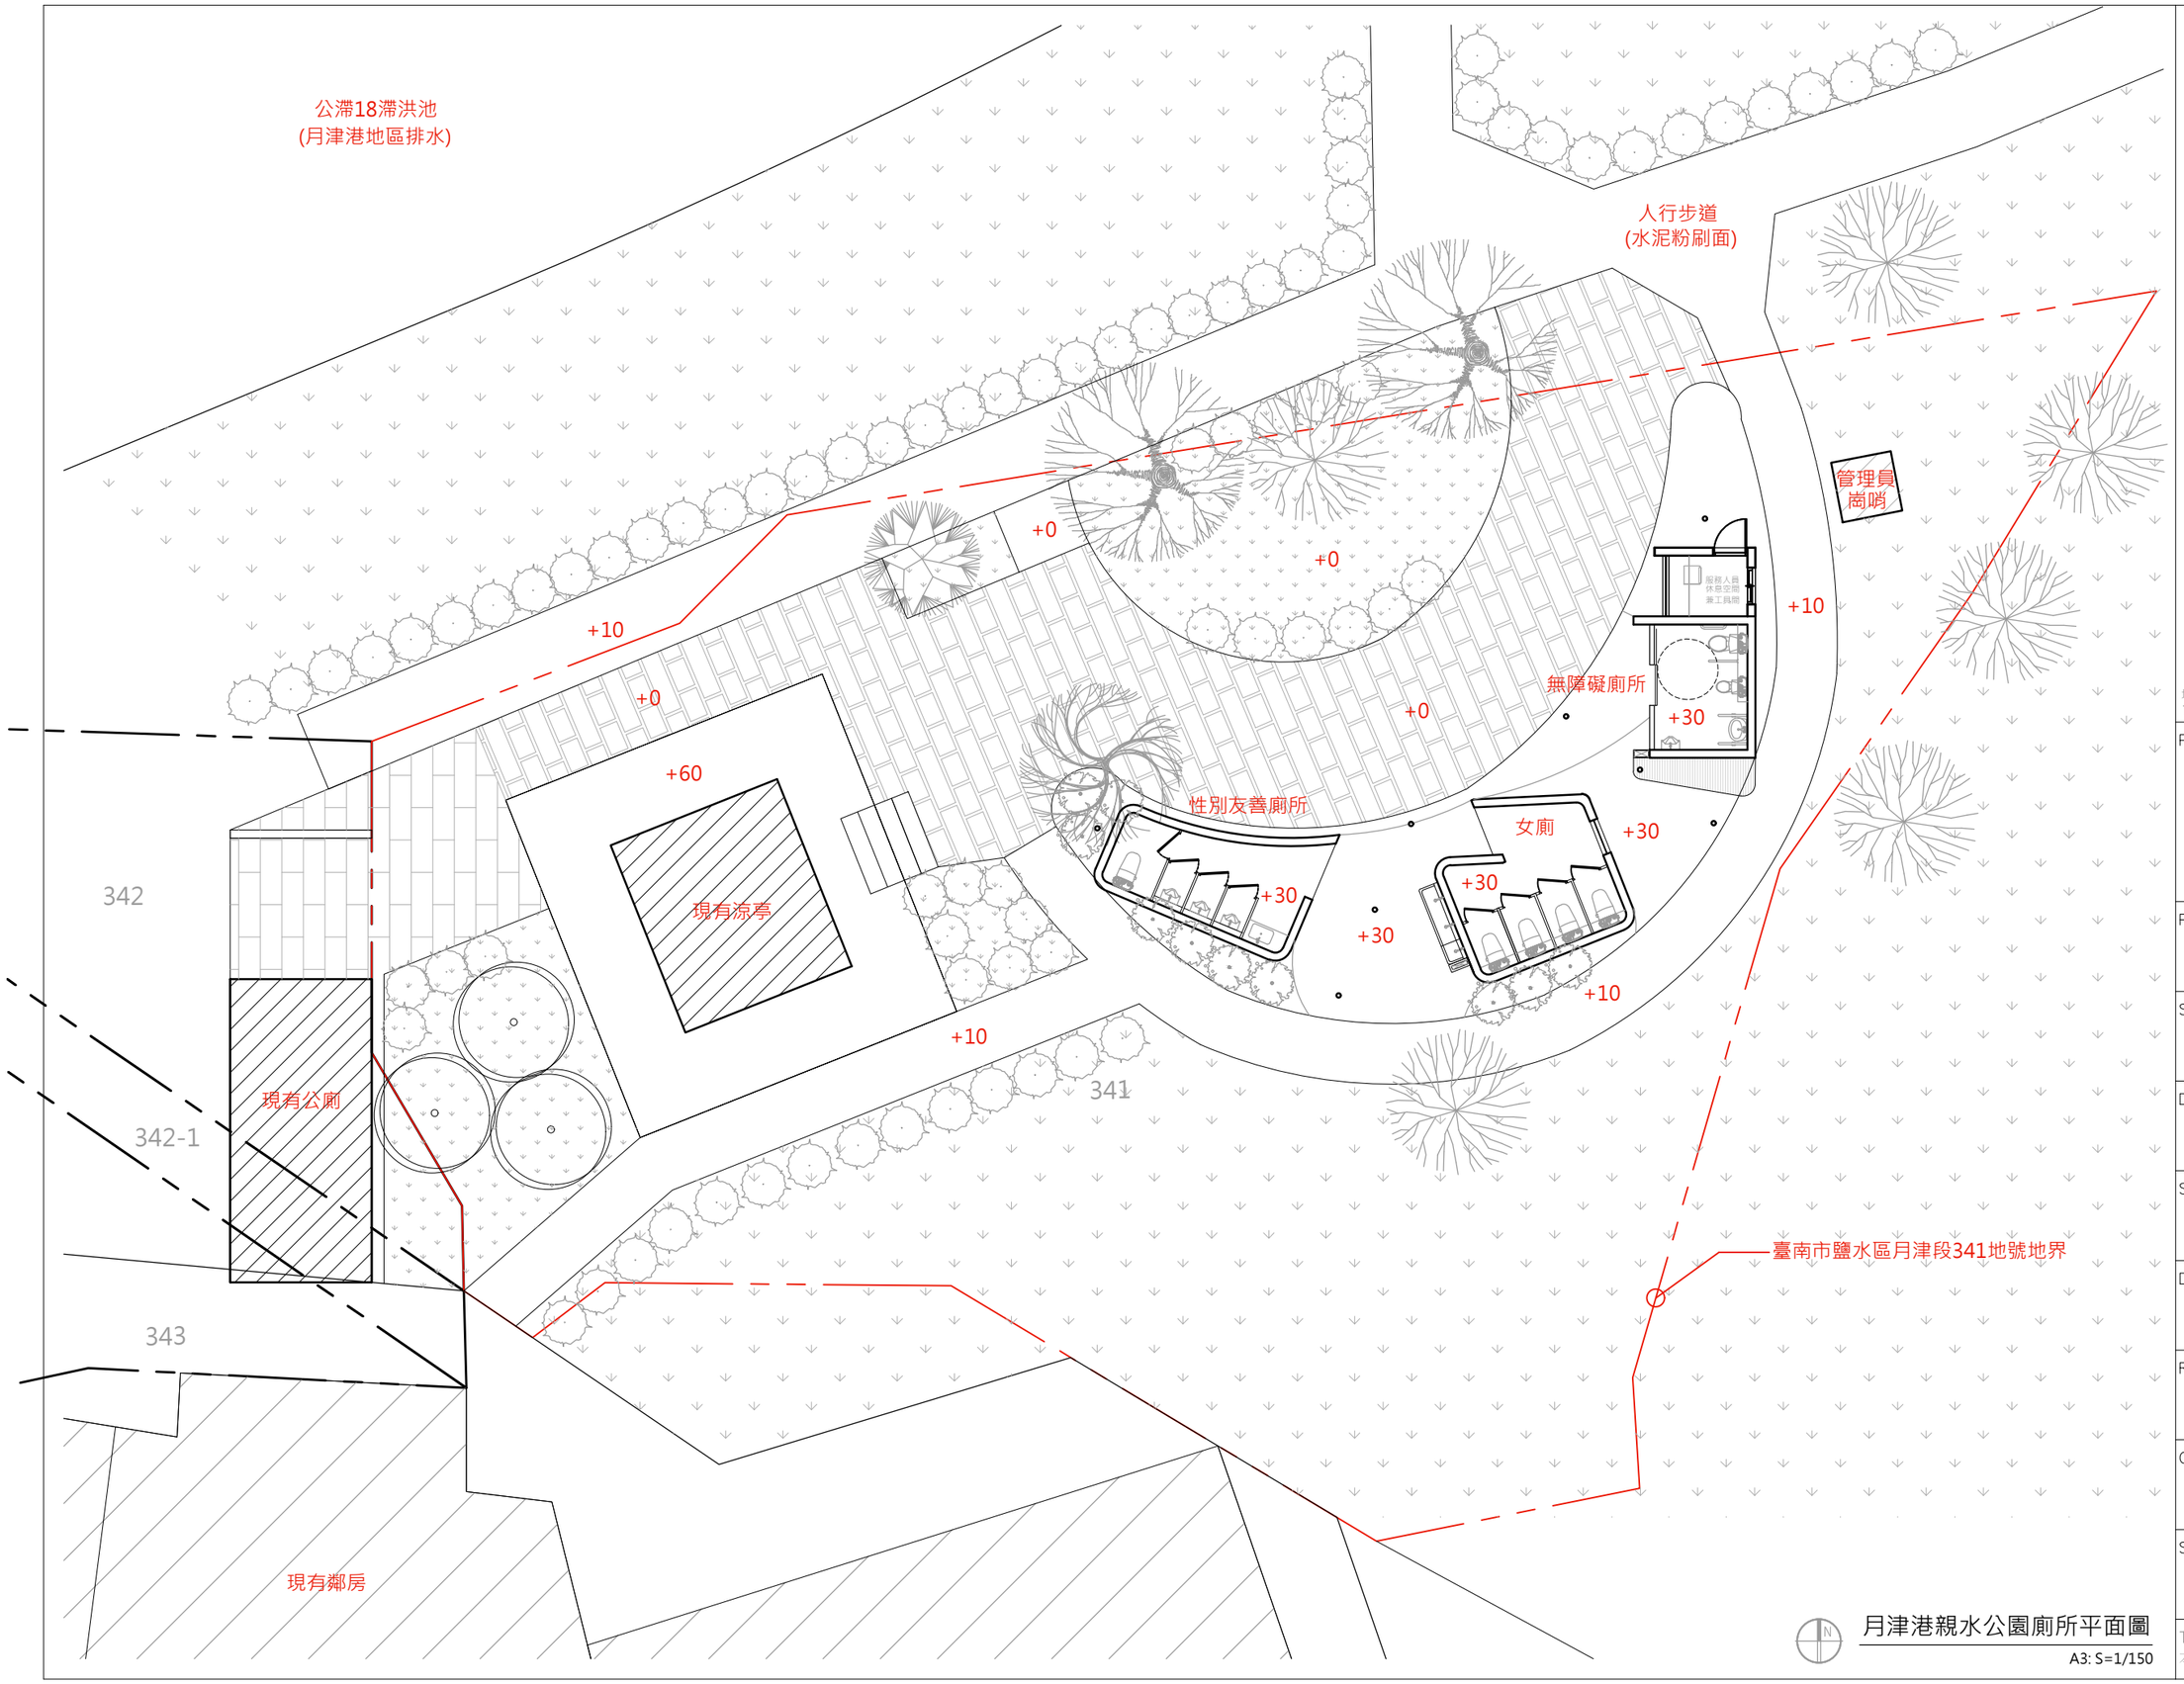

月津港親水公園廁所平面圖
A3: S=1/150

羊門設計與建築
Sheepgate Design & Architecture
+
羊門工程行
地址: 台南市崇善12街6巷15弄2號
Tel: 06-2600846

PROJECT TITLE 案名
臺南市鹽水區
月津港公園公共廁所新建工程

PROJECT NO. 案號
2024-08

SHEET NAME 圖名
月津港親水公園廁所平面圖

DRAWN NO. 圖號
A2-1

SCALE 比例
A3
S:1/150
cm


DATE 日期
202408

REVIEWED 審核確認

CLENT COMFIRM 客戶確認

SHEET NO. 頁碼
--

This drawing is copyright
本圖版權所有

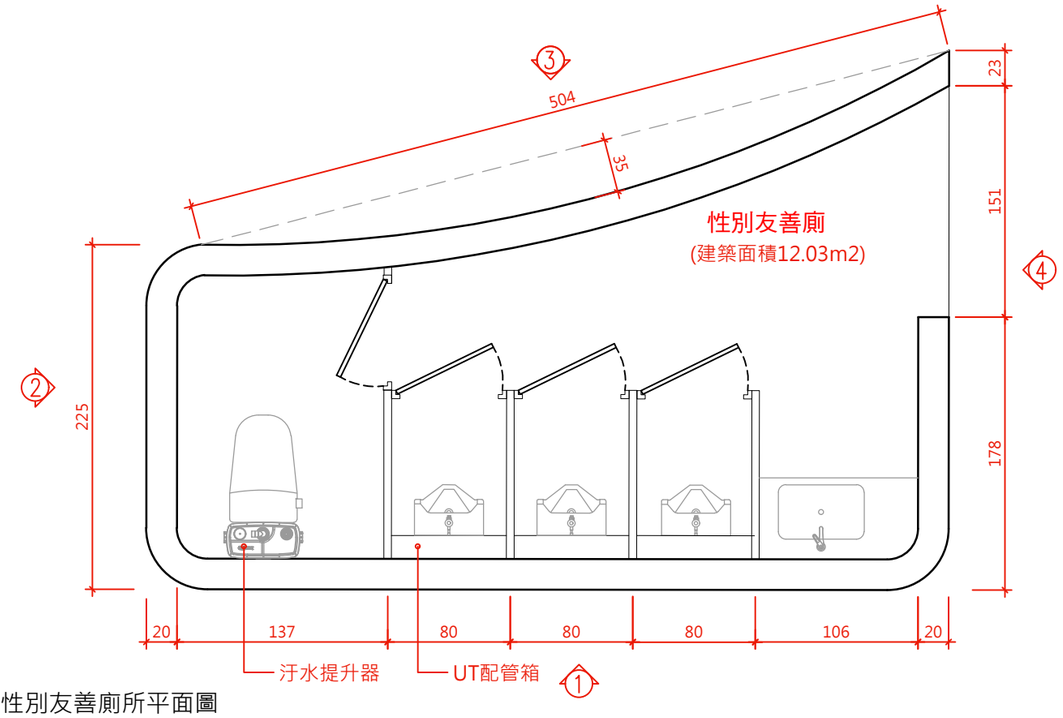

性別友善廁所平面圖

A3: S=1/40

實施都市計畫以外地區建築物管理辦法:

第 6 條

起造人在第三條規定範圍以外之土地，申請興建農舍以外之建築物者 (如興建工廠須先取得工業用地證明書)，應由依法登記開業之建築師設計，向縣 (市) 主管建築機關依建築法規定申請建造執照。

但建築面積在四十五公方公尺以下，建築高度三·五公尺以下者，得免由建築師設計，逕行申請建造執照。

原有建築物之修建、改建或增建面積在四十五平方公尺以下之平房，得免申請建造執照。

本案檢討:


1.本案屬公共設施建築

2.公廁建築面積=12.03+3.6+8.11+13.83=37.57m2 ＜ 45m2

3.建築物高度345cm ＜ 350cm


設備設計說明:

1.本案馬桶採用汙水提升器，減少馬桶於各類活動大量使用，造成堵塞，採機械式動力排放。

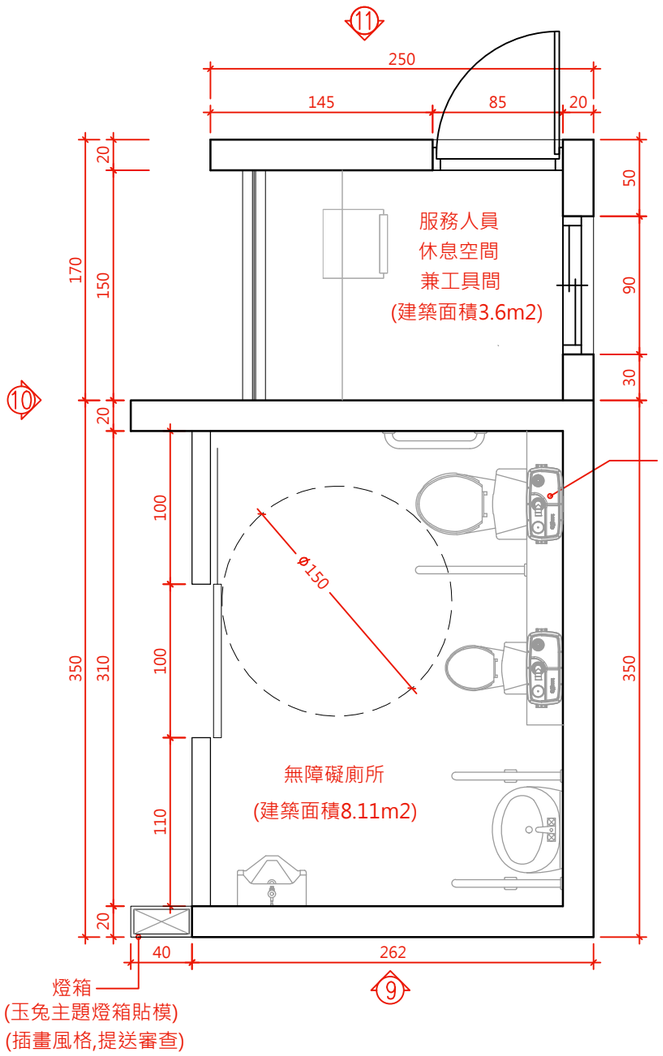

無障礙廁所平面圖

A3: S=1/40

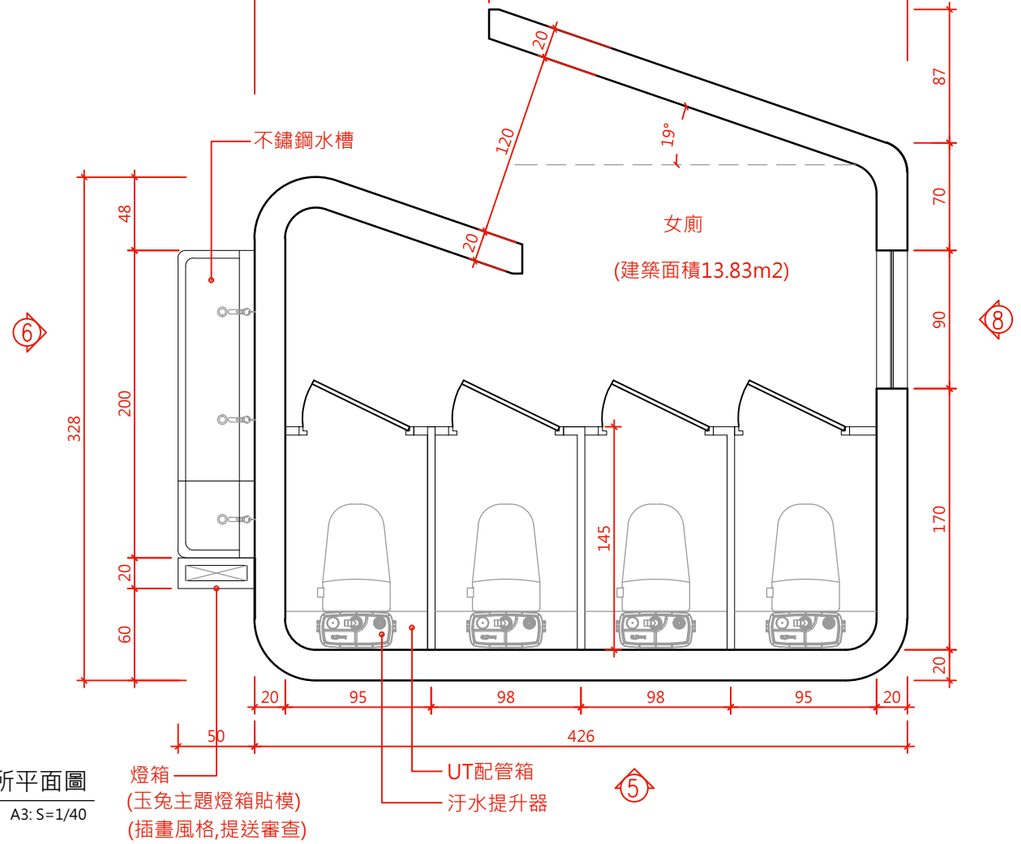

女廁廁所平面圖

A3: S=1/40

羊門設計與建築

Sheepgate Design & Architecture

+

羊門工程行

地址: 台南市崇善12街6巷15弄2號
Tel: 06-2600846

PROJECT TITLE 案名

臺南市鹽水區
月津港公園公共廁所新建工程

PROJECT NO. 案號
2024-08

SHEET NAME 圖名
廁所平面大樣圖

DRAWN NO. 圖號
A2-3

SCALE 比例
A3
S:1/40
cm


DATE 日期
202408

REVIEWED 審核確認

CLENT COMFIRM 客戶確認


SHEET NO. 頁碼
--

This drawing is copyright
本圖版權所有

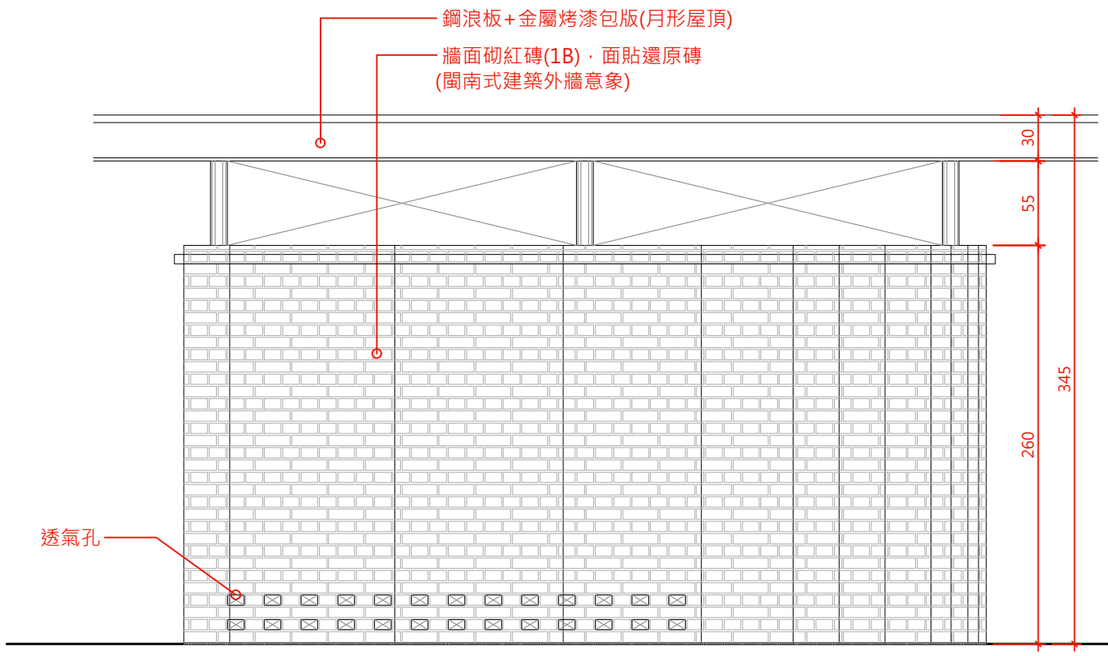


性別友善廁所3立面圖

A3: S=1/40

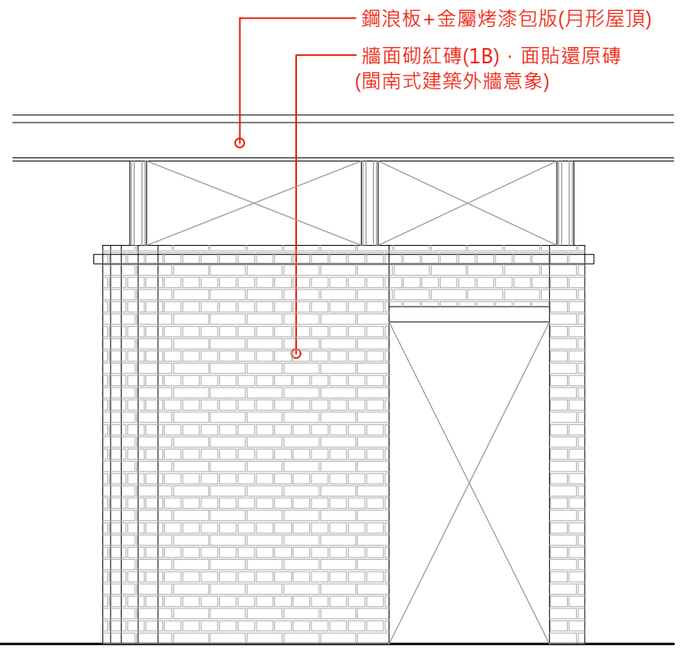


性別友善廁所4立面圖

A3: S=1/40

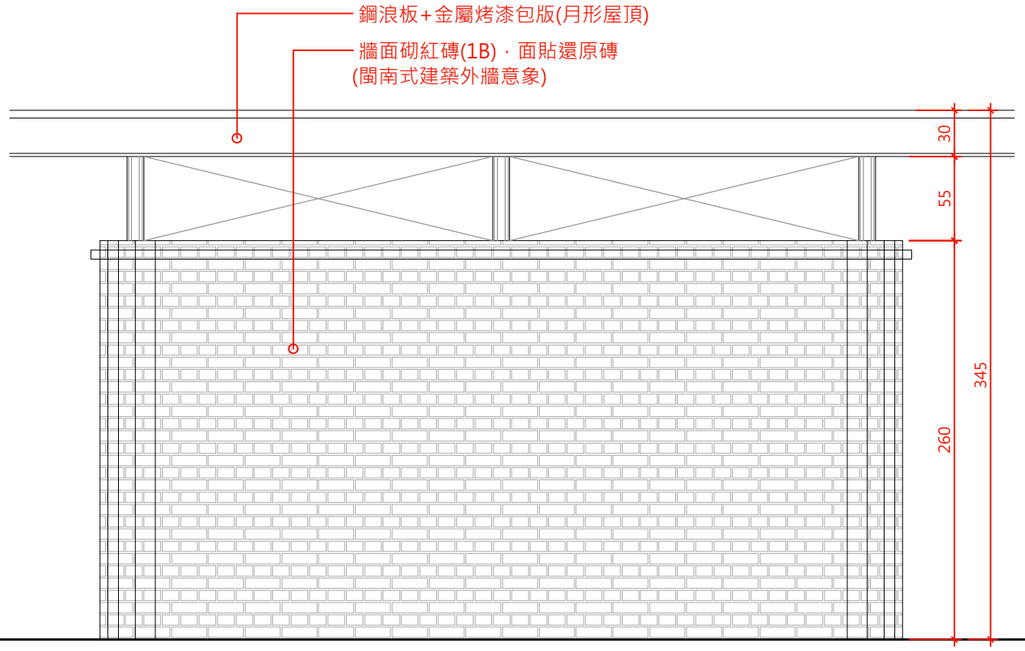

性別友善廁所1立面圖

A3: S=1/40

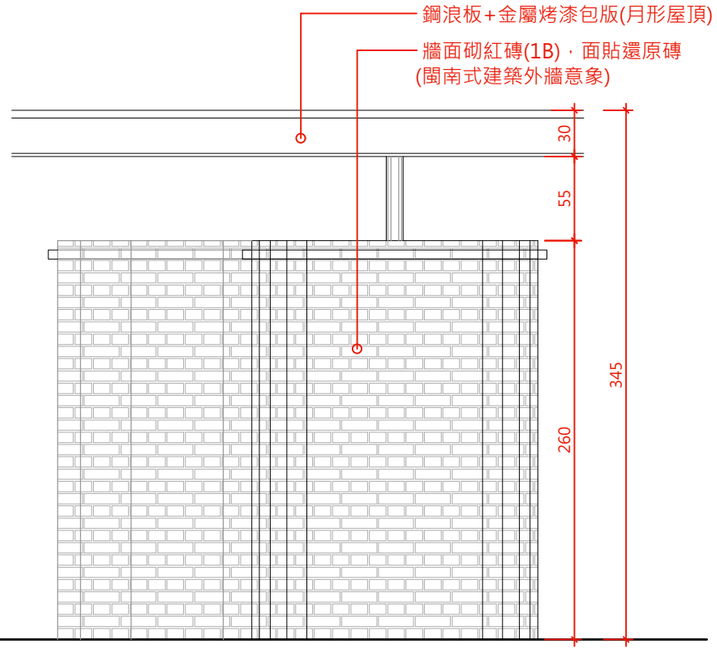

性別友善廁所2立面圖

A3: S=1/40

羊門設計與建築
Sheepgate Design & Architecture
+
羊門工程行

地址: 台南市崇善12街6巷15弄2號
Tel: 06-2600846

PROJECT TITLE 案名

臺南市鹽水區
月津港公園公共廁所新建工程

PROJECT NO. 案號
2024-08

SHEET NAME 圖名
性別友善廁所立面圖

DRAWN NO. 圖號
A3-1

SCALE 比例
A3
S:1/40
cm


DATE 日期
202408

REVIEWED 審核確認

CLENT COMFIRM 客戶確認


SHEET NO. 頁碼
--

This drawing is copyright
本圖版權所有

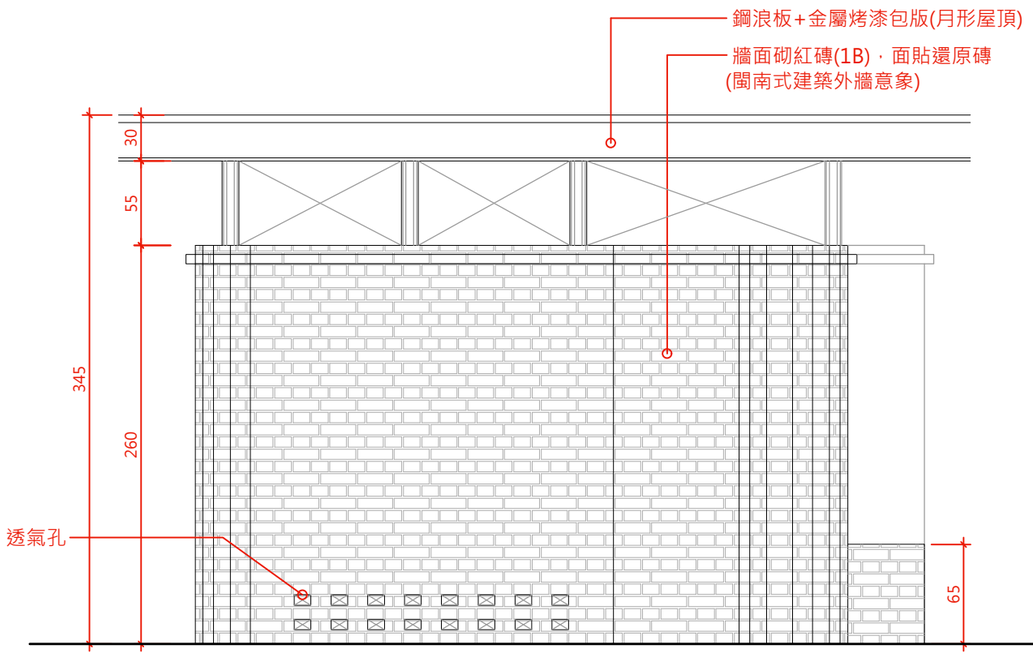


女廁廁所7立面圖

A3: S=1/40

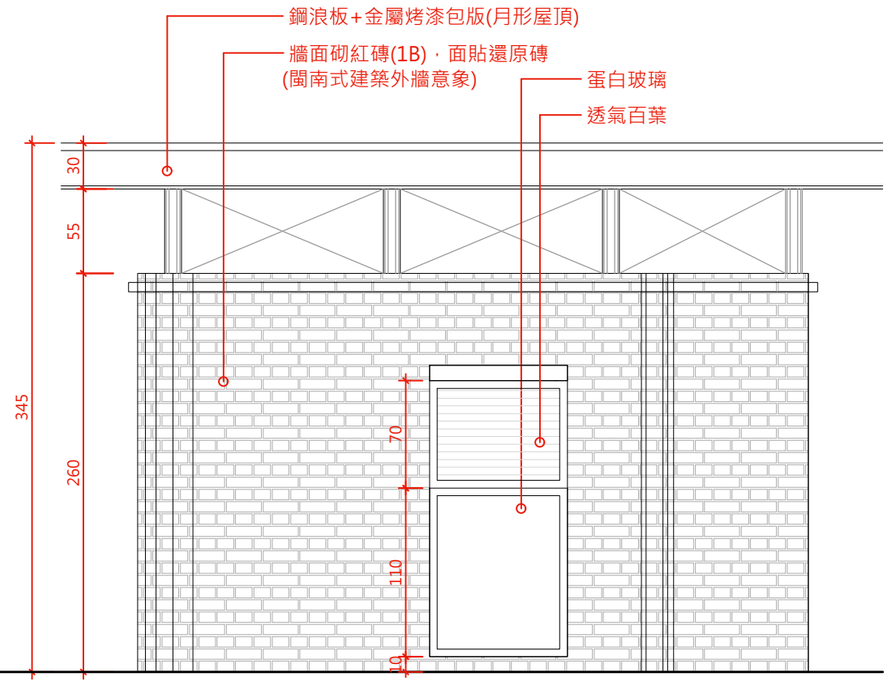


女廁廁所8立面圖

A3: S=1/40

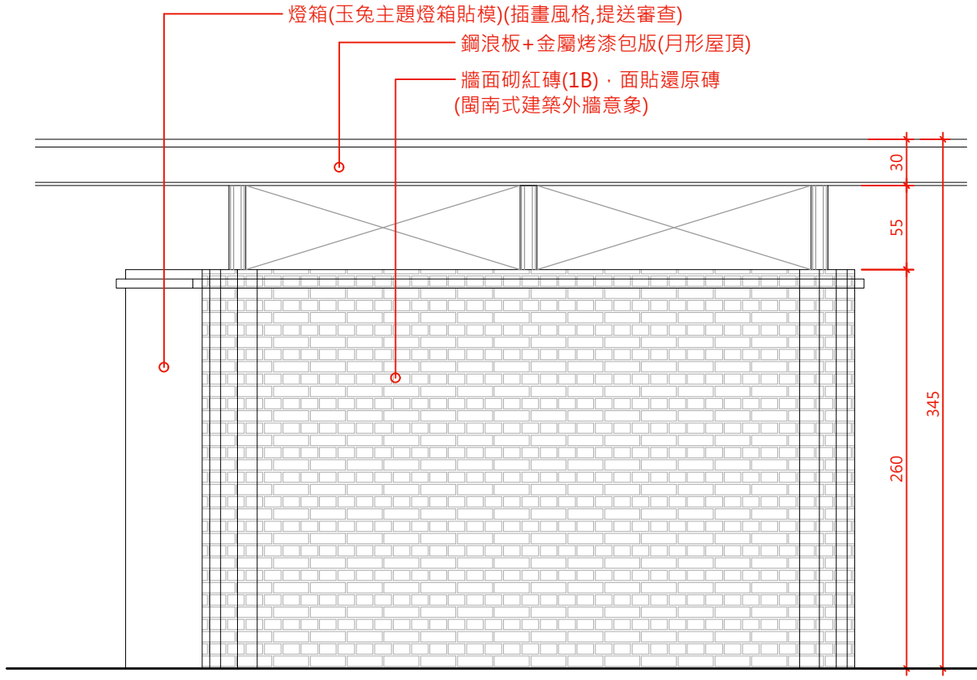

女廁廁所5立面圖

A3: S=1/40

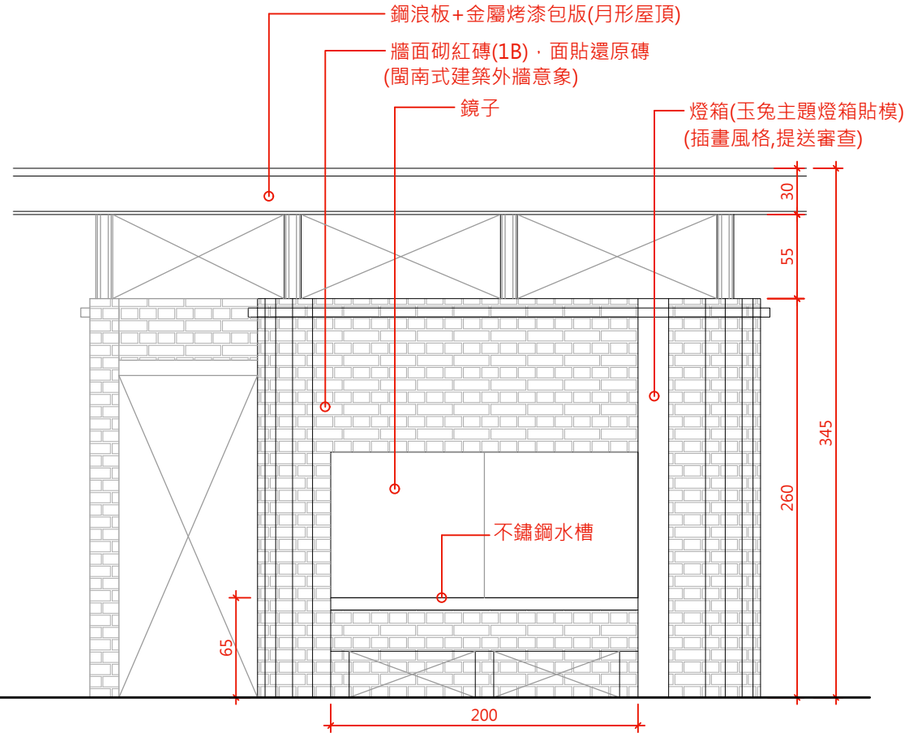

女廁廁所6立面圖

A3: S=1/40

羊門設計與建築
Sheepgate Design & Architecture
+
羊門工程行
地址: 台南市崇善12街6巷15弄2號
Tel: 06-2600846

PROJECT TITLE 案名

臺南市鹽水區
月津港公園公共廁所新建工程

PROJECT NO. 案號
2024-08

SHEET NAME 圖名
女廁廁所立面圖

DRAWN NO. 圖號
A3-2

SCALE 比例
A3
S:1/40
cm


DATE 日期
202408

REVIEWED 審核確認

CLENT COMFIRM 客戶確認


SHEET NO. 頁碼
--

This drawing is copyright
本圖版權所有

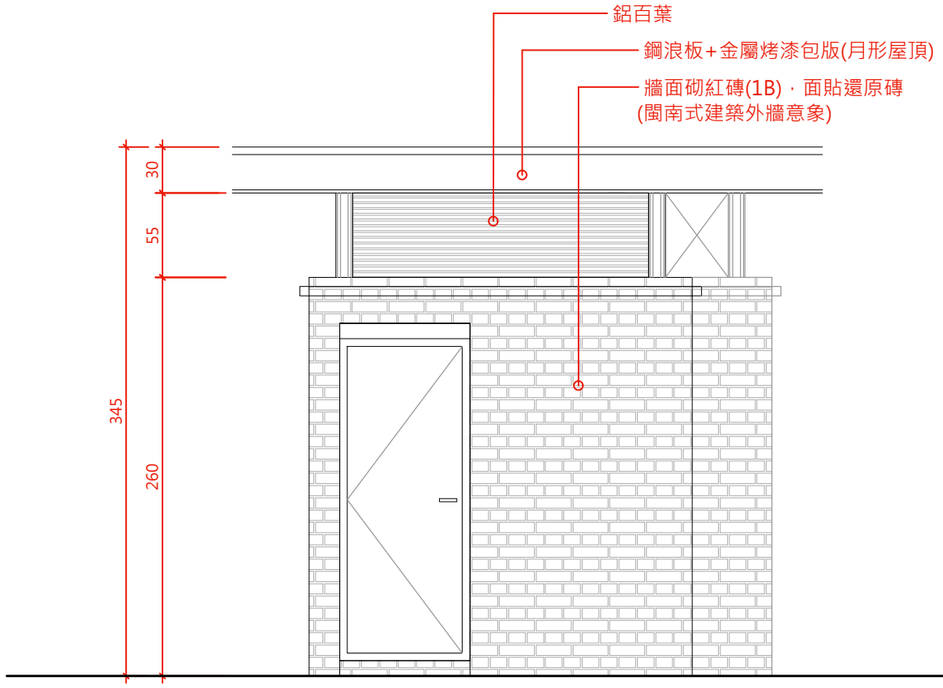


無障礙廁所11立面圖

A3: S=1/40

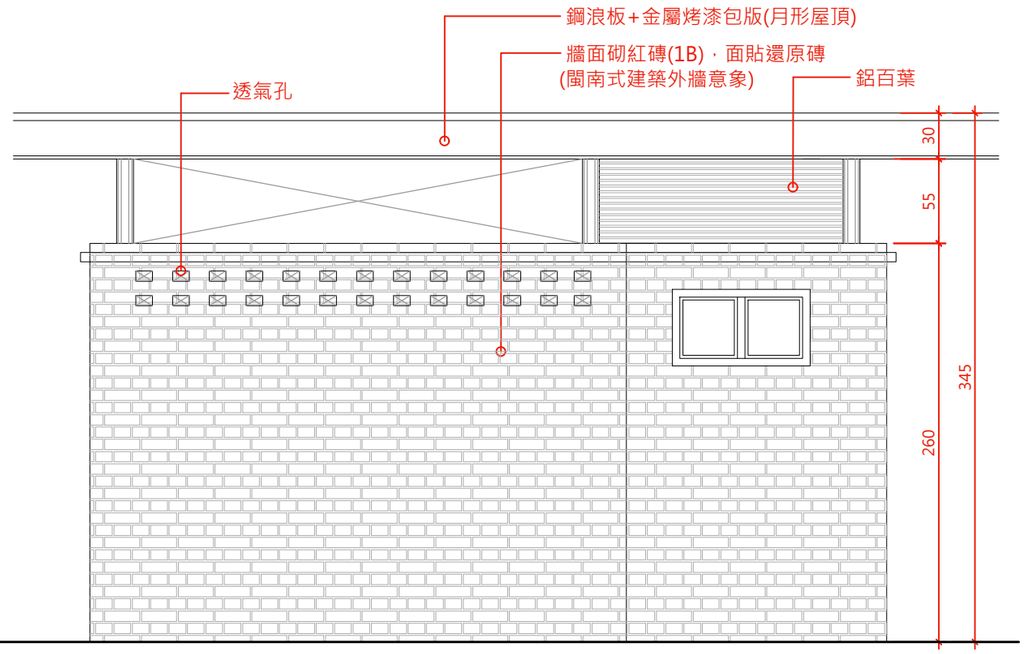


無障礙廁所12立面圖

A3: S=1/40

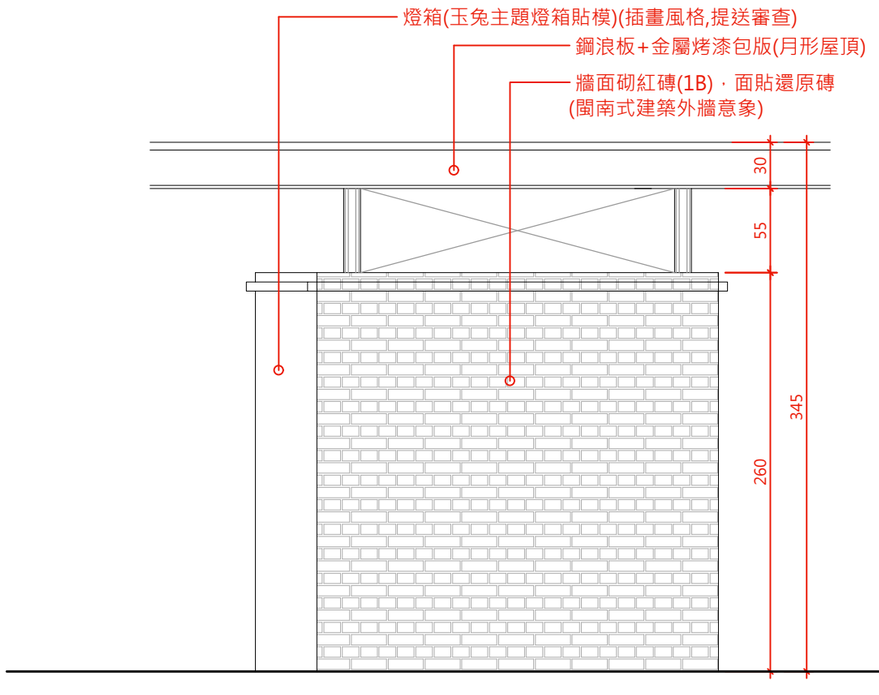

無障礙廁所9立面圖

A3: S=1/40

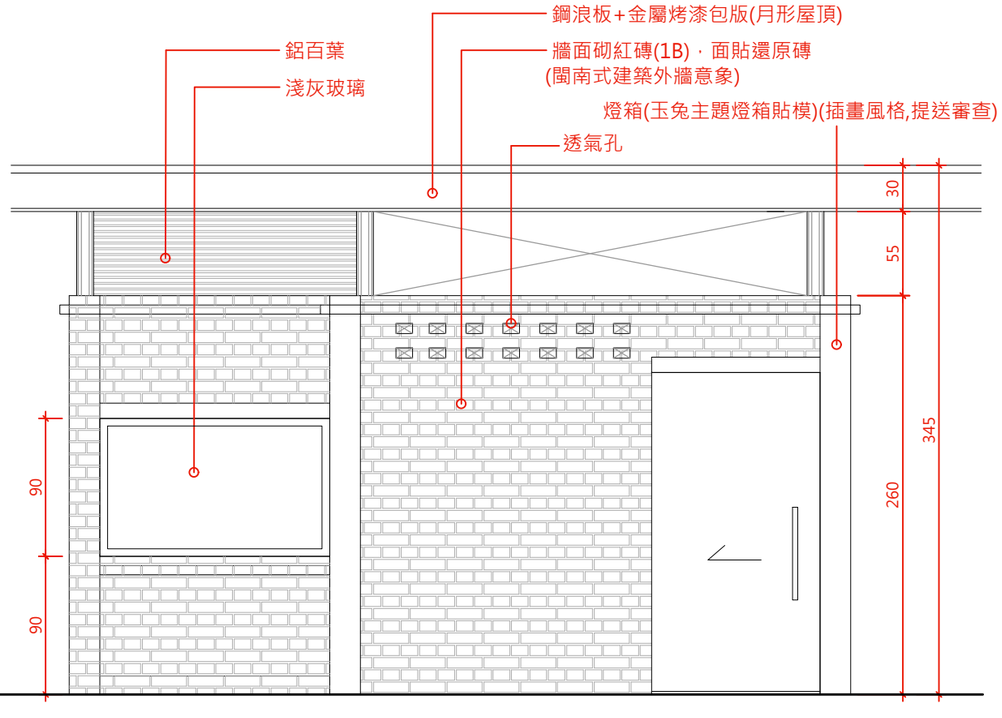

無障礙廁所10立面圖

A3: S=1/40

羊門設計與建築
Sheepgate Design & Architecture
+
羊門工程行

地址: 台南市崇善12街6巷15弄2號
Tel: 06-2600846

PROJECT TITLE 案名

臺南市鹽水區
月津港公園公共廁所新建工程

PROJECT NO. 案號	2024-08
SHEET NAME 圖名	無障礙廁所立面圖
DRAWN NO. 圖號	A3-3
SCALE 比例	A3 S:1/40 cm
DATE 日期	202408
REVIEWED	審核確認
CLENT COMFIRM	客戶確認
SHEET NO. 頁碼	--

This drawing is copyright
本圖版權所有

臺南市政府
詳細價目表[預算]

工程名稱	臺南市鹽水區月津港公園公共廁所新建工程			會計科目		
施工地點	臺南市鹽水區			工程編號		
項 次	項 目 及 說 明	單 位	數 量	單 價	複 價	編碼(備註)
壹	發包工程費					
一	假設工程					
1.1	整地及地上物拆(打)除(含植栽、周邊舊有設施)	式	1.00	124,000	124,000	
1.2	甲種工程圍籬(含夜間警示、門鎖)	式	1.00	262,500	262,500	
1.3	安全圍籬修復及修復地坪損壞部分	式	1.00	90,000	90,000	
1.4	臨時電設置及設備費用	式	1.00	150,000	150,000	
1.5	臨時水設置及設備費用	式	1.00	90,000	90,000	
1.6	點井(積水及淺層地下水抽離)	式	1.00	60,000	60,000	
1.7	臨時活動廁所	式	1.00	48,000	48,000	
1.8	告示牌及安全防護措施	式	1.00	12,000	12,000	
1.9	竣工圖+簽證+上傳主管機關	式	1.00	180,000	180,000	
1.10	道路保護臨時鋼板租賃	式	1.00	90,000	90,000	
1.11	營建廢棄物運棄	式	1.00	160,000	160,000	
	小計(一)				1,266,500	
二	結構工程					
2.1	開挖(挖棄土方)	m^3	30.00	2,000	60,000	淤泥
2.2	回填土方	m^3	224.00	1,300	291,200	GL(-100cm)
2.3	普通模板组立	m^2	25.76	3,000	77,280	1.基礎2.FL+30
2.4	SDW280中拉鋼筋綁紮FY=2800kg/cm^2	T	8.00	26,000	208,000	1.基礎2.FL+30
2.5	SDW420高拉鋼筋綁紮FY=4200kg/cm^2	T	5.00	29,500	147,500	1.基礎2.FL+30
2.6	基礎鏍栓預埋	組	28.00	6,000	168,000	1.基礎
2.7	預拌混擬土壓送澆置140kg/cm^2	m^3	15.00	2,950	44,250	1.基礎2.FL+30
2.8	預拌混擬土壓送澆置280kg/cm^2	m^3	20.00	3,300	66,000	1.基礎2.FL+30
2.9	鋼管鷹架含防護網(符合法規及CNS4750	m^2	180.00	950	171,000	施工範圍
2.10	圓鋼立柱Ø139.6mm(t=3.2mm)(含烤漆)	組	28.00	4,500	126,000	建物支撐
2.11	C型鋼屋面骨架150*75*20*3mm(含異型加工)	T	1.20	55,000	66,000	建物支撐
2.12	預埋螺栓無收縮水泥灌注收邊	式	1.00	30,000	30,000	
2.13	造型屋頂面鋪彩色鋼浪板	m^2	120.00	4,500	540,000	
2.14	造型屋頂底面鋁包版	m^2	120.00	5,800	696,000	
2.15	造型屋頂邊鋼板(不銹鋼螺絲+矽利康施打)	M	60.00	2,350	141,000	
	小計(二)				2,832,230	
三	裝修工程					
3.1	砌磚1B	m^2	123.00	1,200	147,600	
3.2	牆面1：3水泥砂漿打底	m^2	123.00	1,800	221,400	

設計單位

臺南市政府
詳細價目表[預算]

工程名稱	臺南市鹽水區月津港公園公共廁所新建工程			會計科目		
施工地點	臺南市鹽水區			工程編號		
項 次	項 目 及 說 明	單 位	數 量	單 價	複 價	編碼(備註)
3.3	防水工程	m^2	168.00	2,200	369,600	
3.4	貼飾還原磁磚(無填縫、黑泥)	m^2	123.00	1,950	239,850	
3.5	男女廁牆面不透水抿石子	m^2	80.00	2,600	208,000	
3.6	無障礙(性別友善)廁所壁磚30*60	m^2	33.00	2,200	72,600	
3.7	無障礙廁(性別友善)所地坪貼30*30止滑磚	m^2	5.00	4,000	20,000	
3.8	外廊地面不透水抿石子鋪面+邊緣10cm水泥收邊	m^2	65.00	2,600	169,000	
3.9	洗手台砌磚1/2B	座	1.00	15,000	15,000	
3.10	洗手台1：3水泥砂漿打底	座	1.000	8,000	8,000	
3.11	洗手台貼飾還原磚(無填縫、黑泥	座	1.00	15,000	15,000	
3.12	不銹鋼雙水槽	座	1.00	28,000	28,000	
3.13	洗手台明鏡	組	1.00	10,000	10,000	
3.14	無障礙廁(性別友善)所明鏡	組	1.00	4,500	4,500	
3.15	無障礙廁所扶手及五金	組	1.00	20,000	20,000	
3.16	男女廁搗擺隔間及門	m^2	25.00	5,200	130,000	
3.17	無障礙(性別友善)廁所門	組	2.00	20,000	40,000	
3.18	UT配管箱(男廁+女廁)	式	1.00	150,000	150,000	
3.19	採光固定窗雙層灰玻-50*180cm(女廁)	樘	1.00	12,960	12,960	
3.20	採光固定窗雙層灰玻-90*150cm(服務人員休息室)	樘	1.00	19,440	19,440	
3.21	鋁窗50*90cm(服務人員休息室)	樘	1.00	6,480	6,480	
3.22	三合一透氣門85*210cm(服務人員休息室)	樘	1.00	25,704	25,704	
	小計(三)				1,933,134	
四	水電工程					
4.1	基礎汙水系統配置及設備(40人份)	式	1.00	200,000	200,000	
4.2	男女廁給排水系統配置及設備(含水塔加壓機)	式	1.00	250,000	250,000	
4.3	無障礙(性別友善)廁所給排水配置及設備	式	1.00	170,000	170,000	
4.4	全區電力系統配置及設備	式	1.00	600,000	600,000	
4.5	全區照明系統配置及設備	式	1.00	150,000	150,000	
4.6	衛浴設備(凱薩)	式	1.00	118,000	118,000	
4.7	5T水塔(2顆串聯)	式	1.00	68,000	68,000	
	小計(四)				1,556,000	

設計單位