排序02

# 北門區溪底寮部落防護應急工程

5

(部落防護)




◆**辦理依據**：「易淹水地區水患治理計畫」臺南市管區域排水北門地區排水系統規劃報告。

◆**保護對象**：提高溪底寮社區防洪標準及保護人口約1,200人

◆**整治情形**：溪底寮社區主要聯外排水為溪底寮中排3-1，受三寮灣堤外線排水外水頂托，內水無法排除，且整體水流由南向北，致既有側溝排水不及，故於匯流處新設抽水機6cms及新設分洪箱涵、抽水平台，加速聚落內水排除。

◆**用地問題**：主要為農水署公有地、緊鄰私人地待協調。

◆**預期效益**：改善淹水面積約83公頃。







圖例

溪底寮社區　直立式手動閘門　積淹水範圍

排序02

# 北門區溪底寮部落防護應急工程

6

(部落防護)

◆**改善策略**：

受三寮灣堤外線排水迴水頂托影響，故於匯流口設置抽水站，提升排洪量

◆**工程內容**：


- ✓ 新建2cms應急抽水站及附屬設施
- ✓ 防潮閘門1座(1m*1m)


◆**工程經費**：3,200萬元







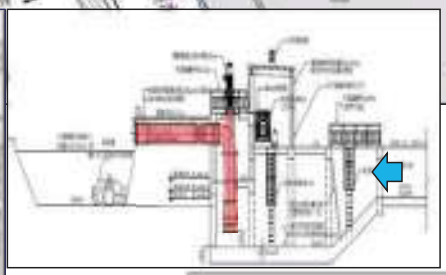

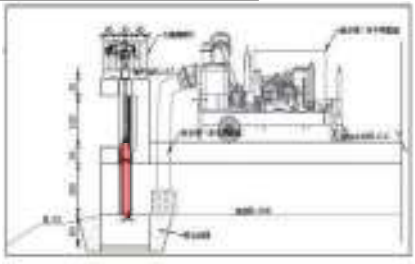

排序03

# 佳里區通興里埔頂社區蒐集水路排水應急工程

7

(排水整治)


改善原因：大寮排水大寮橋兩部0.3cms抽水機，其約14 cms 的逕流量量體不足以完全負荷整體埔頂社區約60 公頃的集水面積

- 工程內容：蒐集水路排水改善432公尺
- 工程經費：約1,000萬元







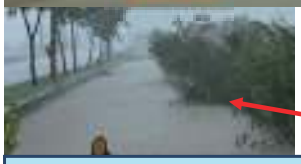


聚落排水系統溢滿



◆辦理依據：大寮排水系統規劃報告
◆保護對象：塭內里
整治情形：目前針對社區採部落蒐集水路，聚落內水經大寮小排一之十一六匯入大寮排水，聚落內新設約432m蒐集水路，藉由增加往南排水流路、減少通興里排水負擔，以改善周圍聚落淹水之情形
◆用地問題：已取得無償同意書
◆預期效益：護岸改善合計約432公尺

■ 斷面示意圖：

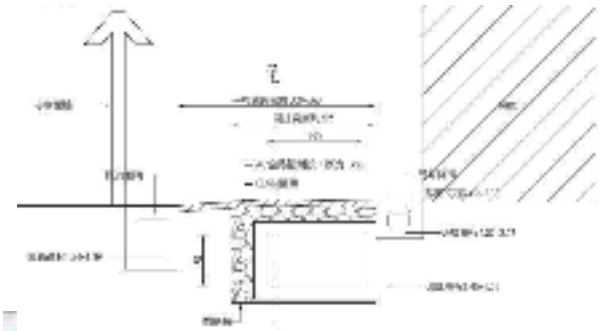




排序4

# 三爺溪排水右岸堤後設施應急工程

8

(水防道路)


◆辦理依據：三爺溪排水系統三爺溪排水及西機場排水治理計畫。
◆保護對象：東區關聖里、文聖里。
◆整治情形：三爺溪水防道路及側溝修復。
◆用地問題：無。
◆預期效益：依據治理計畫原規劃4~6公尺水防道路，辦理水防道路修復利於防汛搶修，以及側溝修復匯集堤後地表逕流，改善積淹水面積約1.5公頃，保護人口約200人。

- 改善原因：無水防道路及側溝。
- 工程內容：水防道路及側溝修復約500公尺
- 工程經費：900萬元。







三爺溪治理計畫水道橫斷面示意圖

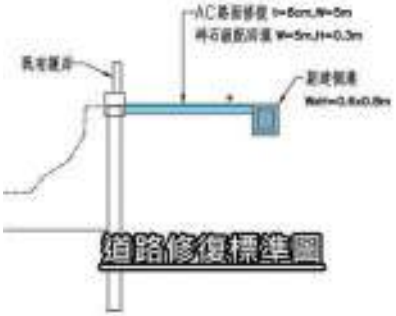

道路修復標準圖

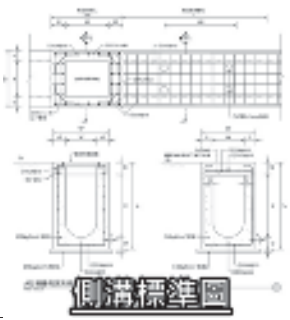

側溝標準圖

排序05

# 北門區北門抽水站機組設備應急工程

9





排序05

# 北門區北門抽水站機組設備應急工程

10

- 工程內容：機組於97年設置已經非常老舊，再加上設計揚程與實際需求有較大的落差，整修恐不符合經濟效益，故更新改善發電機2台、沉水式抽水機6台以及相關控制盤體老舊等項目。
- 工程經費：2,540萬元、技術服務及其它機關費用：360萬元。
- 總需經費：2,900萬元。
- 用地問題：既有抽水站設備更新，無用地問題。
- 預期效益：降低集水區範圍內颱洪期間，災害風險，保護852人及改善淹水面積68公頃。

(機組更新)

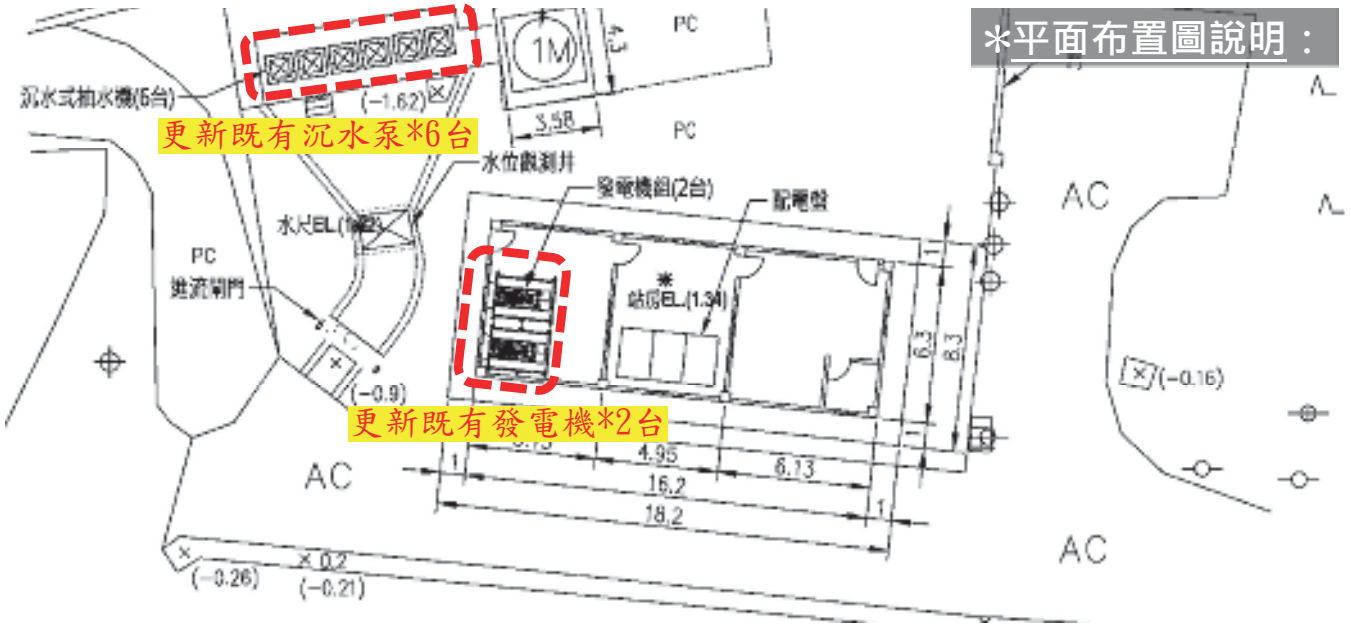

排序06

# 後壁區昇安排水護岸應急工程

11

(排水整治)

◆辦理依據：菁寮排水規劃報告
◆保護對象：土溝里
◆整治情形：目前昇安排水多處為土堤長年受沖刷多處塌陷針對土堤段進行治理
◆用地問題：皆為農水署土地
◆預期效益：土堤改善合計約180公尺，保護1000人及改善淹水面積30公頃





排序06

# 後壁區昇安排水護岸應急工程

12

(排水整治)

- 改善原因：既有護岸為土坡且防洪高度不足
- 工程內容：排水路改善180公尺(兩岸合計360公尺、高度約3.2m)
- 工程經費：2,000萬元

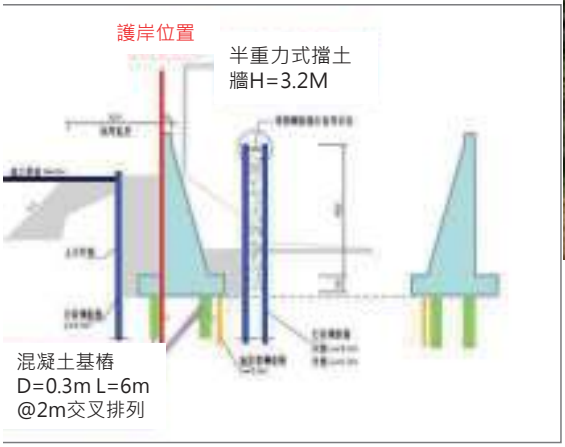







- 斷面示意圖：

排序08

# 北門區38號水門應急工程

13

(防潮閘門)

- 工程內容：直提式閘門W1.65*H1.00*1扇老舊更新，增設自動閘*1扇
- 工程經費：1025萬元、技術服務及其它機關費用：175萬元
- 總需經費：1200萬元
- 用地問題：既有閘門更新，無用地問題
- 預期效益：降低集水區範圍內颱洪期間，災害風險，保護852人及改善淹水面積68公頃




排序09

# 麻豆區安西里前班小排二排水應急工程

14

(排水整治)

- 改善原因：既有砌石溝防洪高度不足
- 工程內容：矩形溝改善120公尺(3m*1.5m)、版橋3處
- 工程經費：600萬元







排序10

# 麻豆區總爺排水支流應急工程

15

(排水整治)

- 改善原因：既有土堤防洪高度不足
- 工程內容：排水路改善100公尺(雙岸合計200公尺，h=3m)
- 工程經費：1,200萬元








排序11


# 龜子港排水抽水設備應急工程

16

(抽水設備)

- 工程內容：增設龜子港排水抽水設備2cms抽水機組，以補足八老爺建議抽水量能(規劃8cms)。本次再增設1組抽水機組2cms(含柴油引擎、角齒輪減速機、離合器及機電配合等設施)等改善工程
- 工程經費：1,000萬元、技術服務及其它機關費用：150萬元
- 總需經費：1,150萬元
- 用地問題：既有抽水站設備增設，無用地問題
- 預期效益：增置2cms抽水機組，保護1600人及改善淹水面積420公頃

*平面布置圖說明：

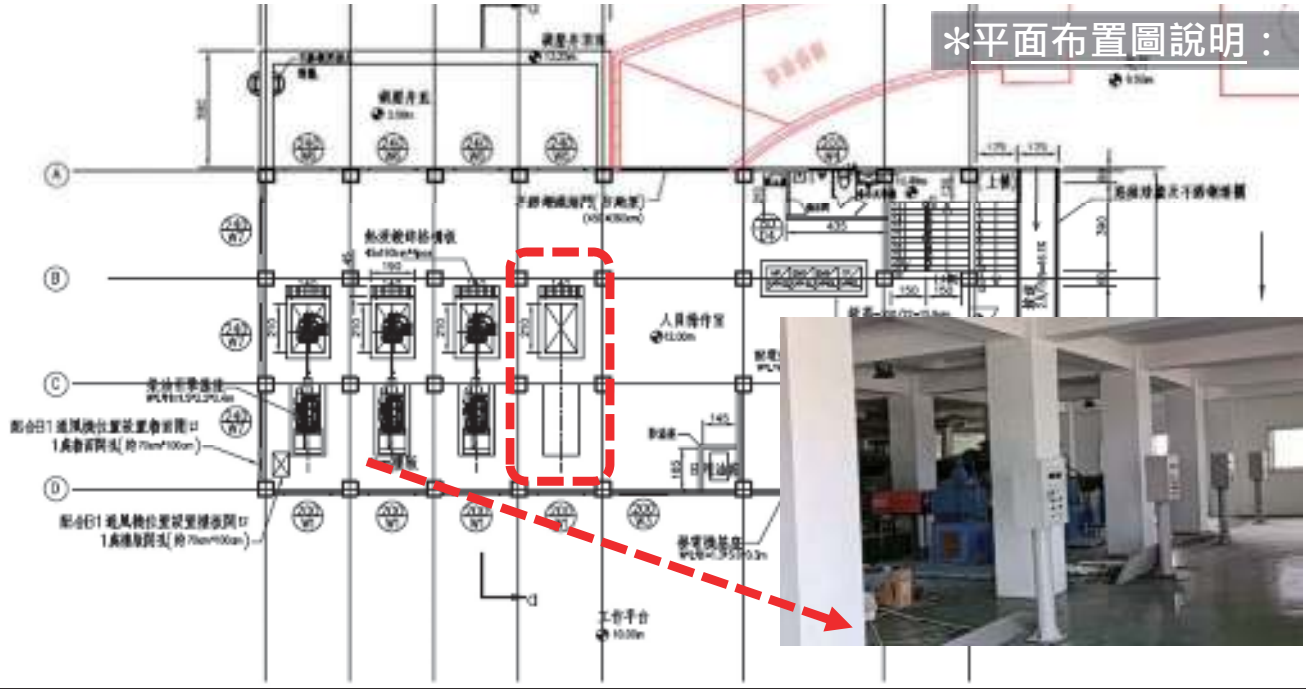

排序12

# 七股區36-1號水門應急工程

17

(防潮閘門)

- 工程內容：閘門現況為雙層四孔自動水門，因角度較為垂直且分為上下兩層，水密性不佳而影響自動水門功能。本案預計於堤內新設2孔直提式閘門，每孔1.25*H3.00，電動吊門機2組 ，周邊護岸銜接及復舊，並整修既有自動水門提高水密性
- 工程經費：985萬元、技術服務及其它機關費用：171萬元
- 總需經費： 1,156萬元
- 用地問題：既有閘門更新，無用地問題
- 預期效益： 保護1000人及改善淹水面積53公頃










排序13

# 麻豆區小埤社區排水應急工程

18

(排水整治)

- 改善原因：既有矩形溝通水斷面不足
- 工程內容：排水路配合國有地改善240公尺(4m*2m)
- 工程經費：1,200萬元









排序14

# 學甲區紅茄萣排水抽水平台應急工程(抽水設備)



◆辦理依據：錦湖排水規劃報告
◆保護對象：北門白米、新渡子頭、學甲紅蝦港、新芳、紅茄萣
◆整治情形：紅茄萣排水部分土堤，渠道寬度足夠，白米紅蝦港落圍堤完成。
◆用地問題：無用地問題。
◆預期效益：保護300人及改善淹水面積60公頃

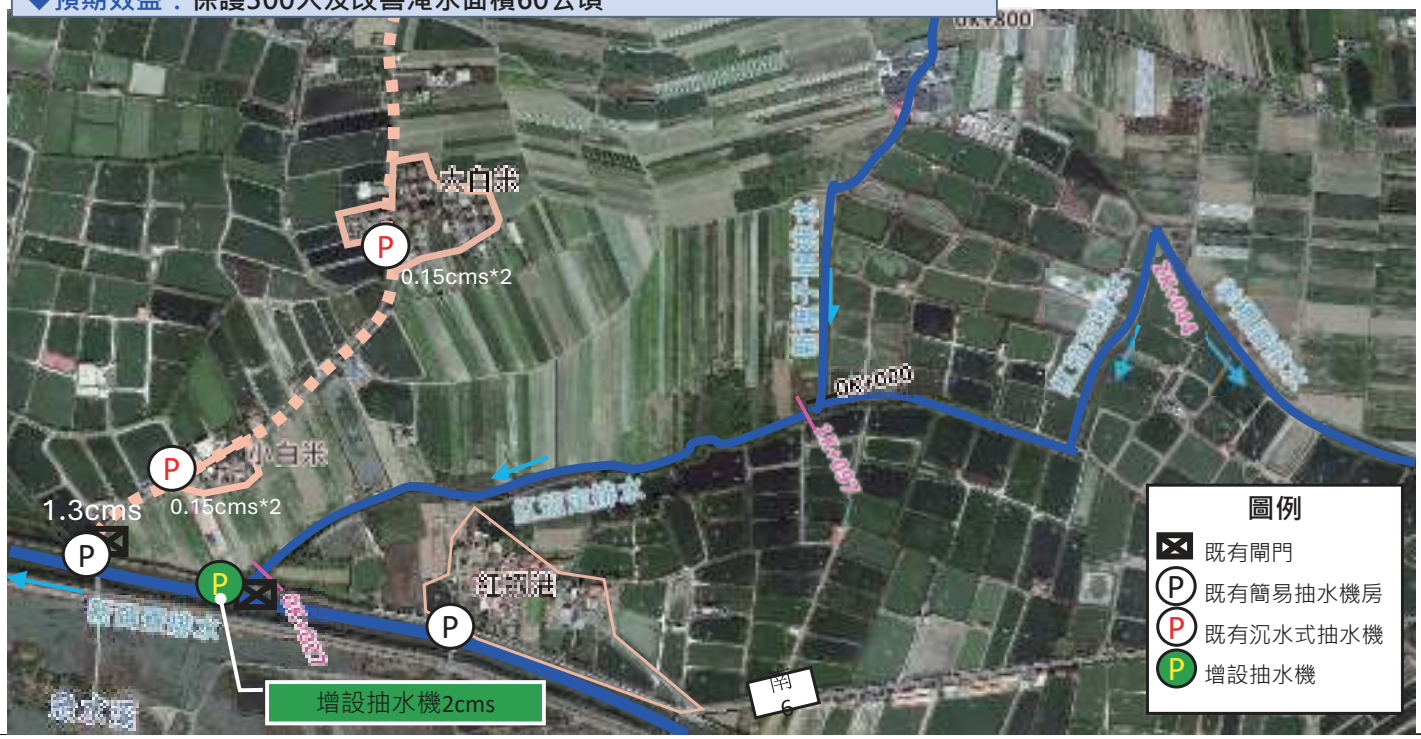



排序14


# 學甲區紅茄萣排水抽水平台應急工程(抽水設備)



- 工程內容：抽水平台(2cms)、調節井1處
- 主要工項：
  ① 集水井W*L*H
  3.5m*13m*2m
  ② 平台及機房1座
  ③ 束軸1cms兩部及出水管件2套
- 工程經費：2,500萬元



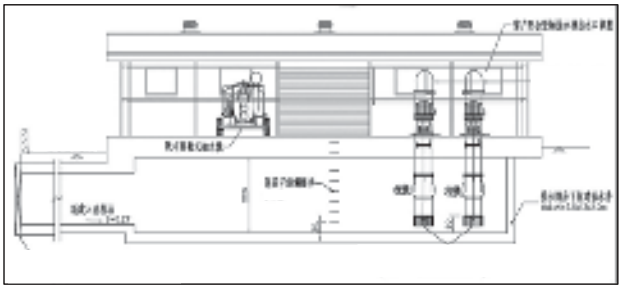

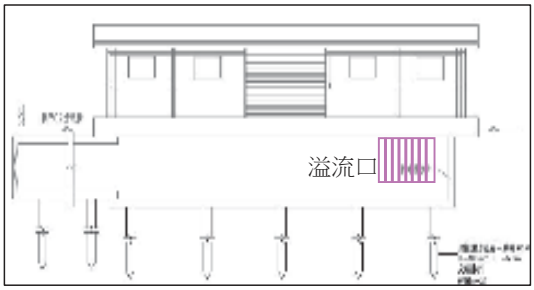
溢流口示意圖



排序15

# 安定區港口中抽水設備擴增應急工程

21

◆保護對象：安定區港口里、港南里

◆整治情形：

- 安順寮排水本段已整治加高完畢，惟高水位期間聚落內水無法排放
- 已設置3cms抽水站，於外水高漲協助將聚落低地逕流藉由機械抽排，避免災害
- 惟考量集水區Q10約4.2cms，建議增設1部1cms抽水機以提升堤後排水效率

◆用地問題：既有站體擴充，屬公有地

◆預期效益：加速港口、港南里聚落排水效率，改善聚落淹水情形



凱米颱風7/25淹水狀況




排序15

# 安定區港口中抽水設備擴增應急工程


22

□工程內容：

- 1cms抽水機組(含抽排水鋼管、舌閥)：1部
- 機電設備擴充與程式編撰
- 抽水站平台擴建
- 撈污機檢修通道

□工程經費：1,000萬元

| 項次 | 工程項目 | 單位 | 數量 | 單價(萬元) | 複價(萬元) |
|---|---|---|---|---|---|
| 一 | 直接工作費 | | | | |
| 1 | 100HP抽水機組(抽水量1cms，含抽、排水鋼管 | 組 | 1 | 400.00 | 400 |
| 2 | 機電設備擴充與程式編撰 | 組 | 1 | 140.00 | 140 |
| 3 | 抽水平台擴建 | 座 | 1 | 50.00 | 50 |
| 4 | 撈污機檢修通道 | 座 | 1 | 20.00 | 20 |
| 5 | 臨時工項(約上述10%) | 式 | 1 | 61.00 | 61 |
| 6 | 雜項工程(職安品管利潤稅費約前述20%) | 式 | 1 | 134.00 | 134 |
| 二 | 間接工作費(設監工管空污試驗約壹.一項15%) | 式 | 1 | 115.00 | 115 |
| 工程費用小計 | | | | | 920 |
| 用電契約擴充費用 | | | | | 80 |
| 總工程費合計 | | | | | 1,000 |

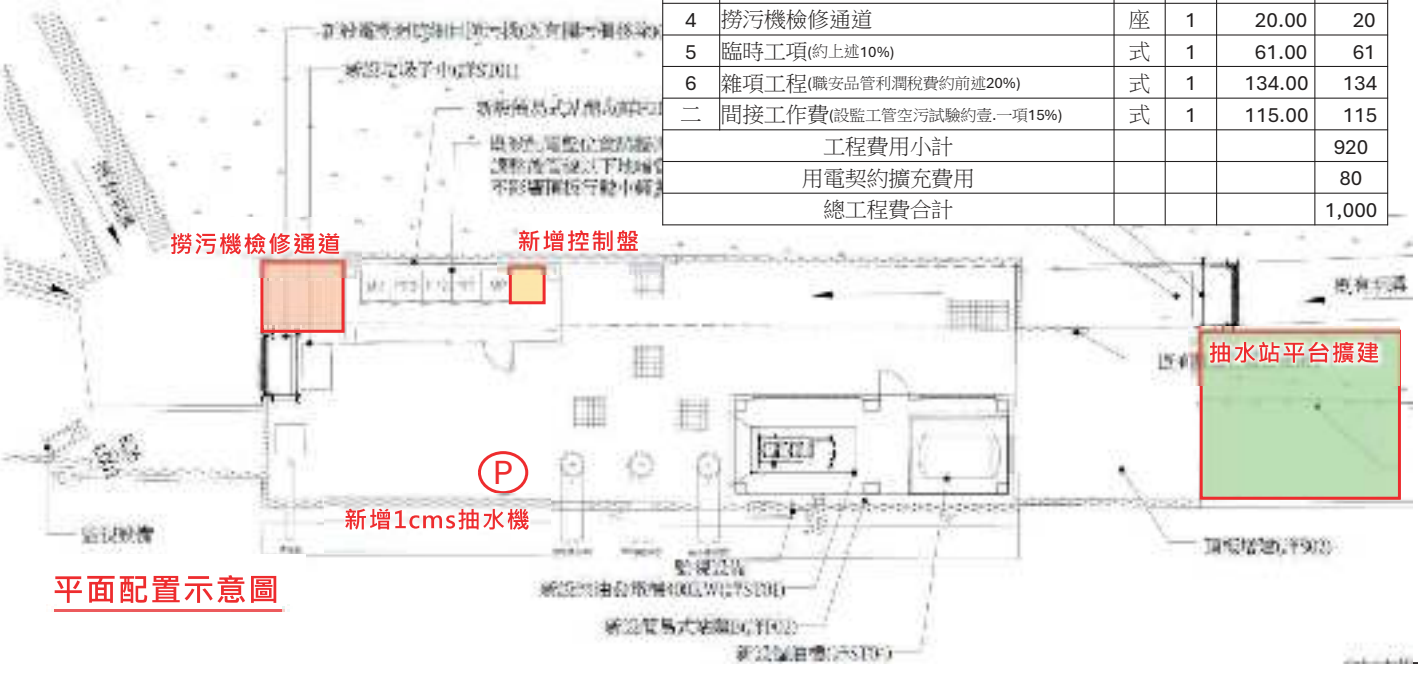


平面配置示意圖

排序16

# 安定區中榮里抽水設備應急工程

23

◆保護對象：安定區中榮里

◆整治情形：

- 聚落主要由聯外排水明溝收集側溝逕流，往東穿越國一後匯入看西排水
- 聚落地勢相對低窪，為避免外水倒灌，已於高速公路西側設置抽水平台及自動閘門
- 本次建議調整抽水平台位置，提升聚落保護效益，並整建收集水路，增加集水效率

◆用地問題：原溝渠改建，屬公有地

◆預期效益：加速中榮里聚落排水效率，改善聚落淹水情形








中榮里淹水情形

排序16

# 安定區中榮里抽水設備應急工程


24

□工程內容：

- 抽水平台改建：1座
- 自動閘門增設：1座
- 進水渠道改建：160m
- AC道路復舊：160m

□工程經費：1,300萬元

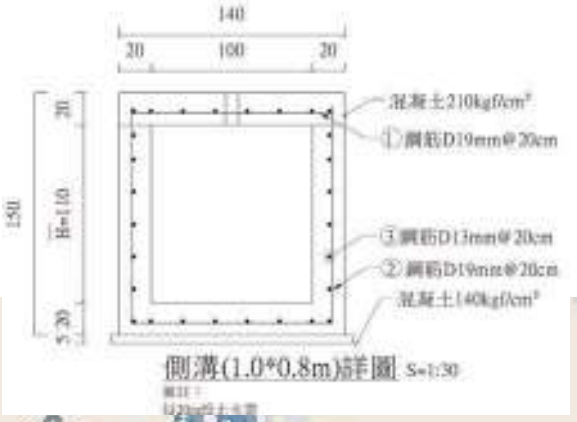


側溝(1.0*0.8m)詳圖 S=1:30

| 項次 | 工程項目 | 單位 | 數量 | 單價(萬元) | 複價(萬元) |
|---|---|---|---|---|---|
| 一 | 直接工作費 | | | | |
| 1 | 抽水平台改建 | 座 | 1 | 60.00 | 60 |
| 2 | 新設自動閘門[3*2m，含附屬設備] | 座 | 1 | 120.00 | 120 |
| 3 | 入流渠道改建 | m | 160 | 2.00 | 320 |
| 5 | 既設RC渠道拆除與運棄 | m | 160 | 0.60 | 96 |
| 6 | 臨時擋土鋼軌樁與鋼板 | m | 320 | 0.20 | 64 |
| 8 | 道路刨除與運棄[W=4m，t=5cm] | t | 92 | 0.15 | 14 |
| 9 | 道路修復W=4m[t=5cm] | m2 | 800 | 0.05 | 40 |
| 10 | 樹木移植 | 株 | 2 | 10.00 | 20 |
| 11 | 鄰房鑑定[一層門牌/單元] | 單元 | 12 | 0.80 | 10 |
| 12 | 鄰房監測 | 戶 | 4 | 2.00 | 8 |
| 13 | 交通維持人員 | 式 | 1 | 100.00 | 100 |
| 14 | 臨時工項[以上10%] | 式 | 1 | 85.00 | 85 |
| 15 | 雜項工程[含管理費及利潤20%] | 式 | 1 | 187.00 | 187 |
| 二 | 間接工作費[含施工管理費、污染防治措施費、一般15%] | 式 | 1 | 177.00 | 177 |
| | 工程費用小計 | | | | 1,300 |